


GAS REGULATOR PLATE

PLATE NO.
15-U-R

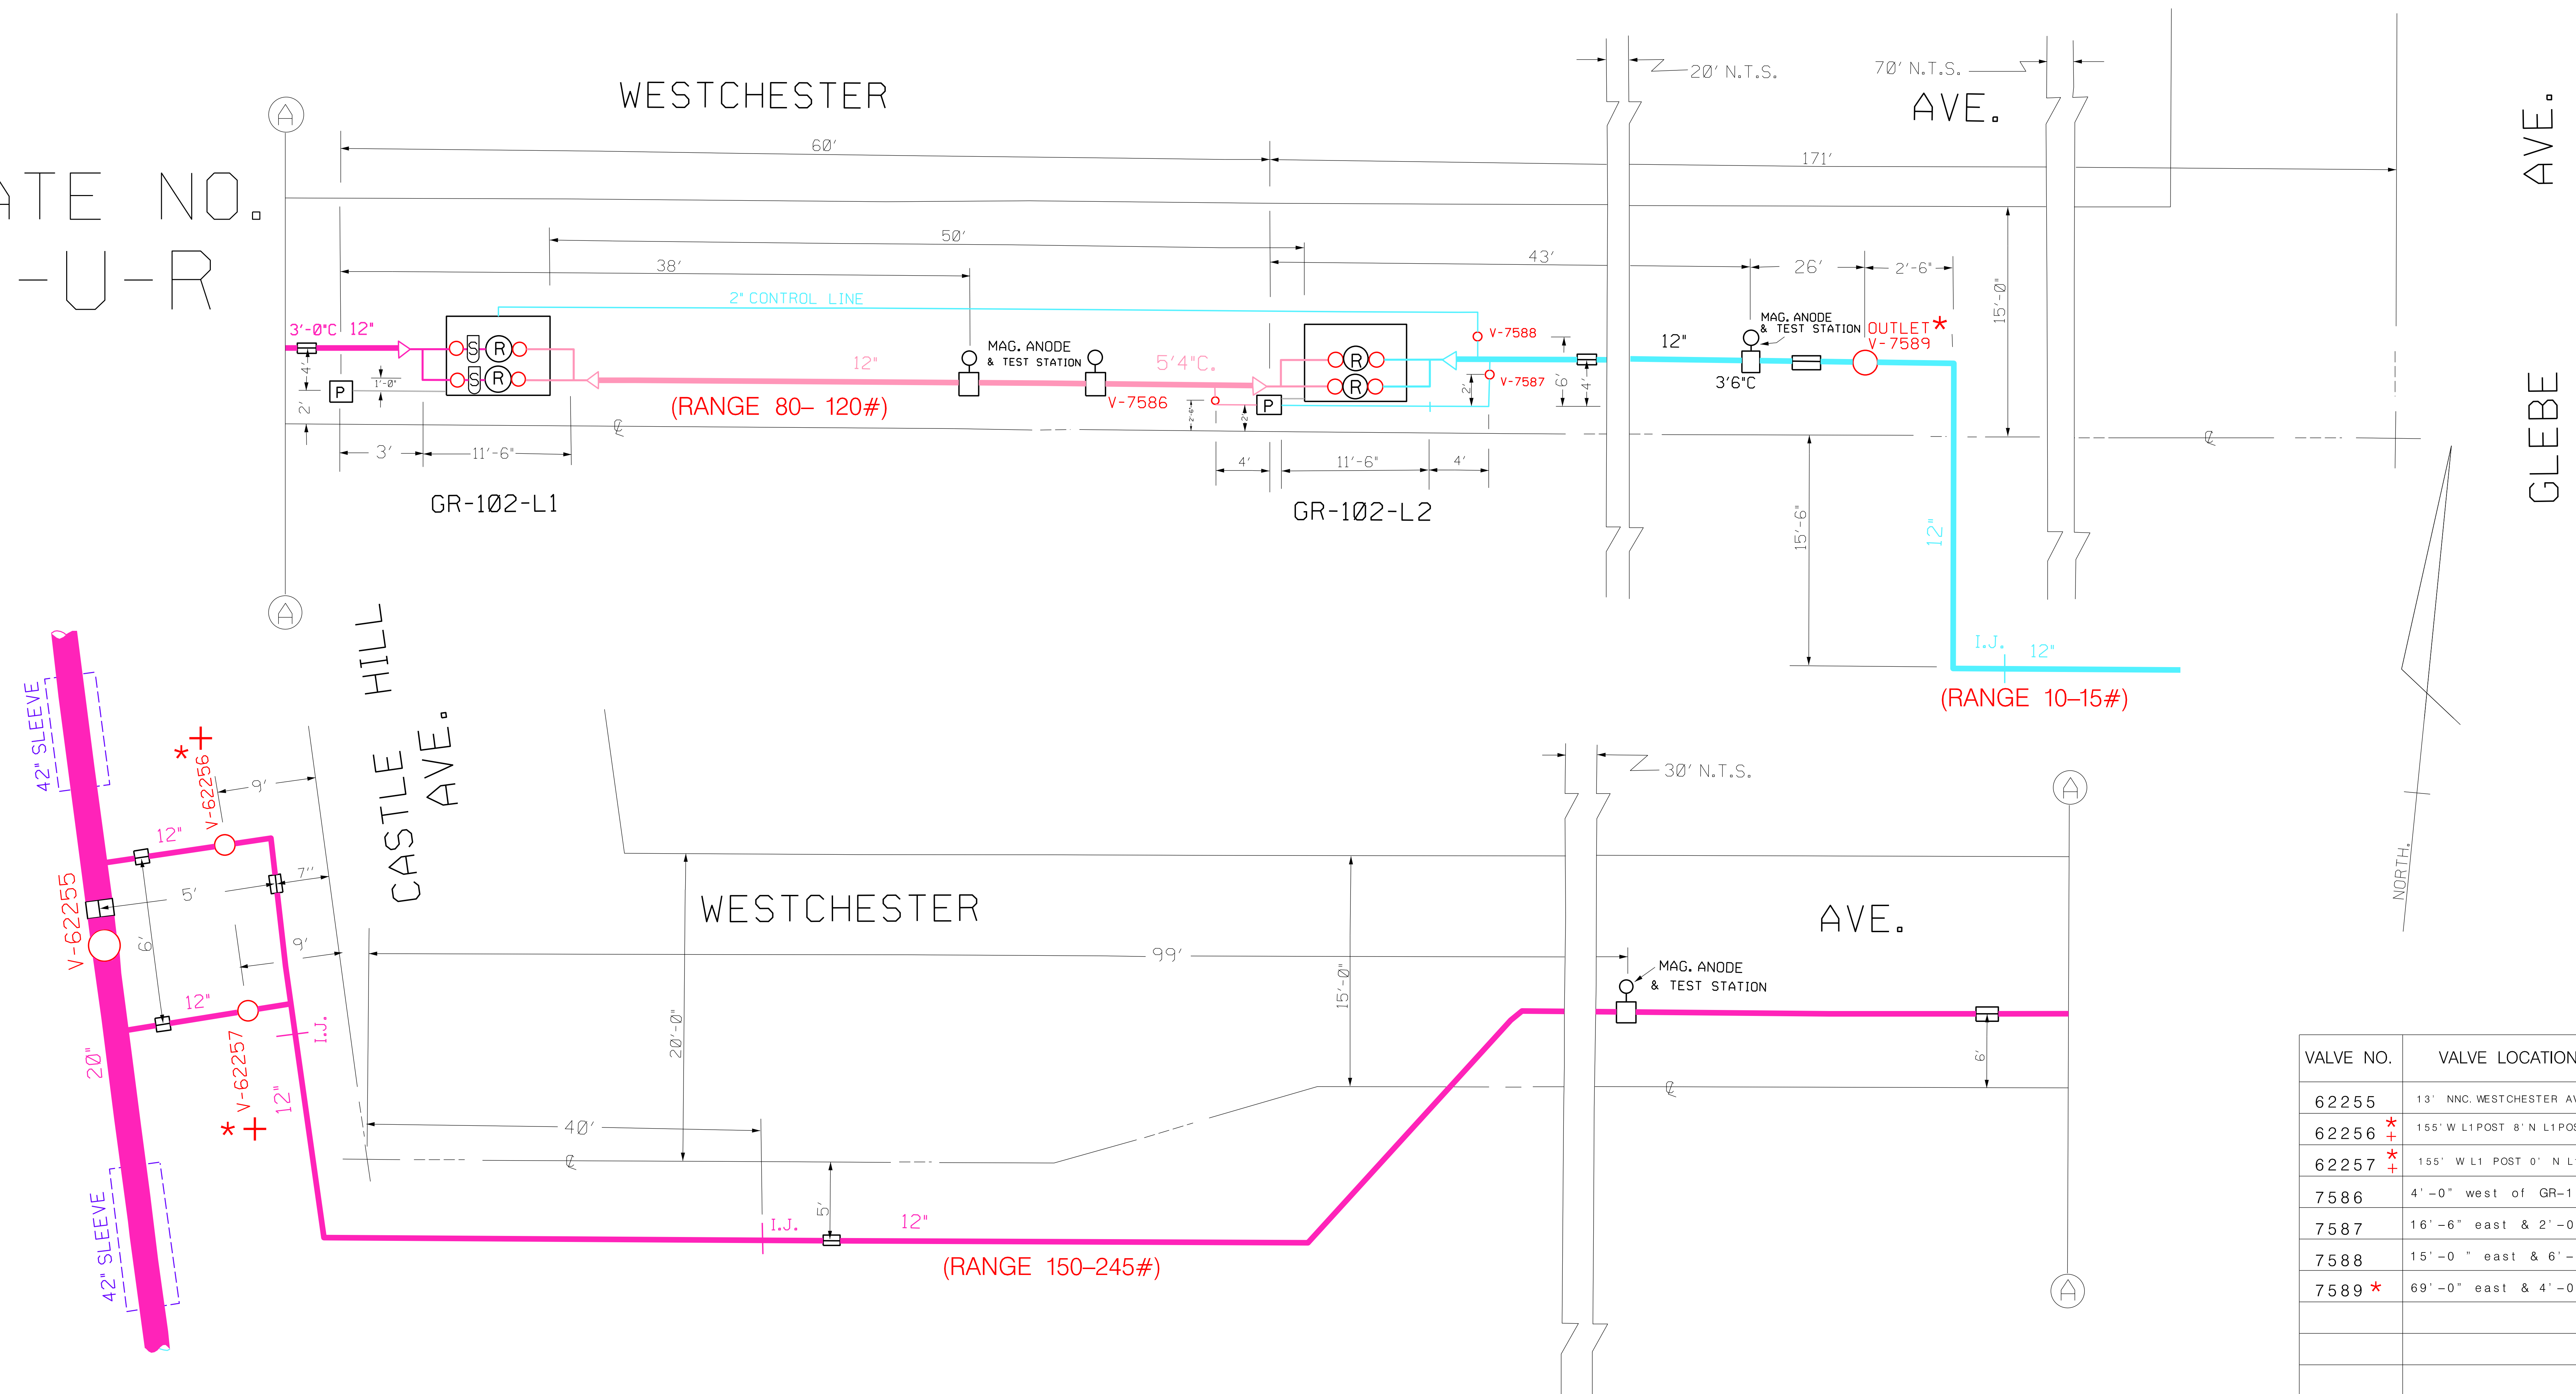

VALVE NO.	VALVE LOCATION FROM GAUGE POST
62255	13' NNC WESTCHESTER AV. & 12' WEC. CASTLE HILL AV.
62256   	155' W L1 POST 8' N L1 POST
62257   	155' W L1 POST 0' N L1 POST
7586	4' -0" west of GR-102-L2
7587	16' -6" east & 2' -0" north of GR-102-L2
7588	15' -0 " east & 6' -0" north of GR-102-L2
7589 	69' -0" east & 4' -0" north of GR-102-L2

* = PRINCIPAL STATION VALVE
INSPECTED AND PARTIALLY
OPERATED ANNUALLY.

+ = TRANSMISSION VALVE
(ANY VALVE THAT SEES
PRESSURE ABOVE 125 PSIG)
INSPECTED AND PARTIALLY
OPERATED ANNUALLY.

ANY VALVE OPERATION OR MAINS CUT OUT IN THE
AREA SHOWN ABOVE MAY AFFECT OPERATION OF
THIS DISTRICT REGULATOR. THE CENTRAL GAS
CONTROLLER AND THE MANAGER OF PRESSURE CONTROL
MUST BE NOTIFIED IN ADVANCE OF THIS WORK.

STRAINER INFORMATION				
	SIZE	BODY RATING	MANUFACTOR	MODEL
L1 N	4"	300 #	MUESSCO	
L1 S	4"	300 #	MUESSCO	

[illegible][illegible]

LOCATION: WESTCHESTER AVE. WEST OF GLEBE AVE.		GR-102M
OPERATING MAP 15-U	GENERAL MAINS MAP	