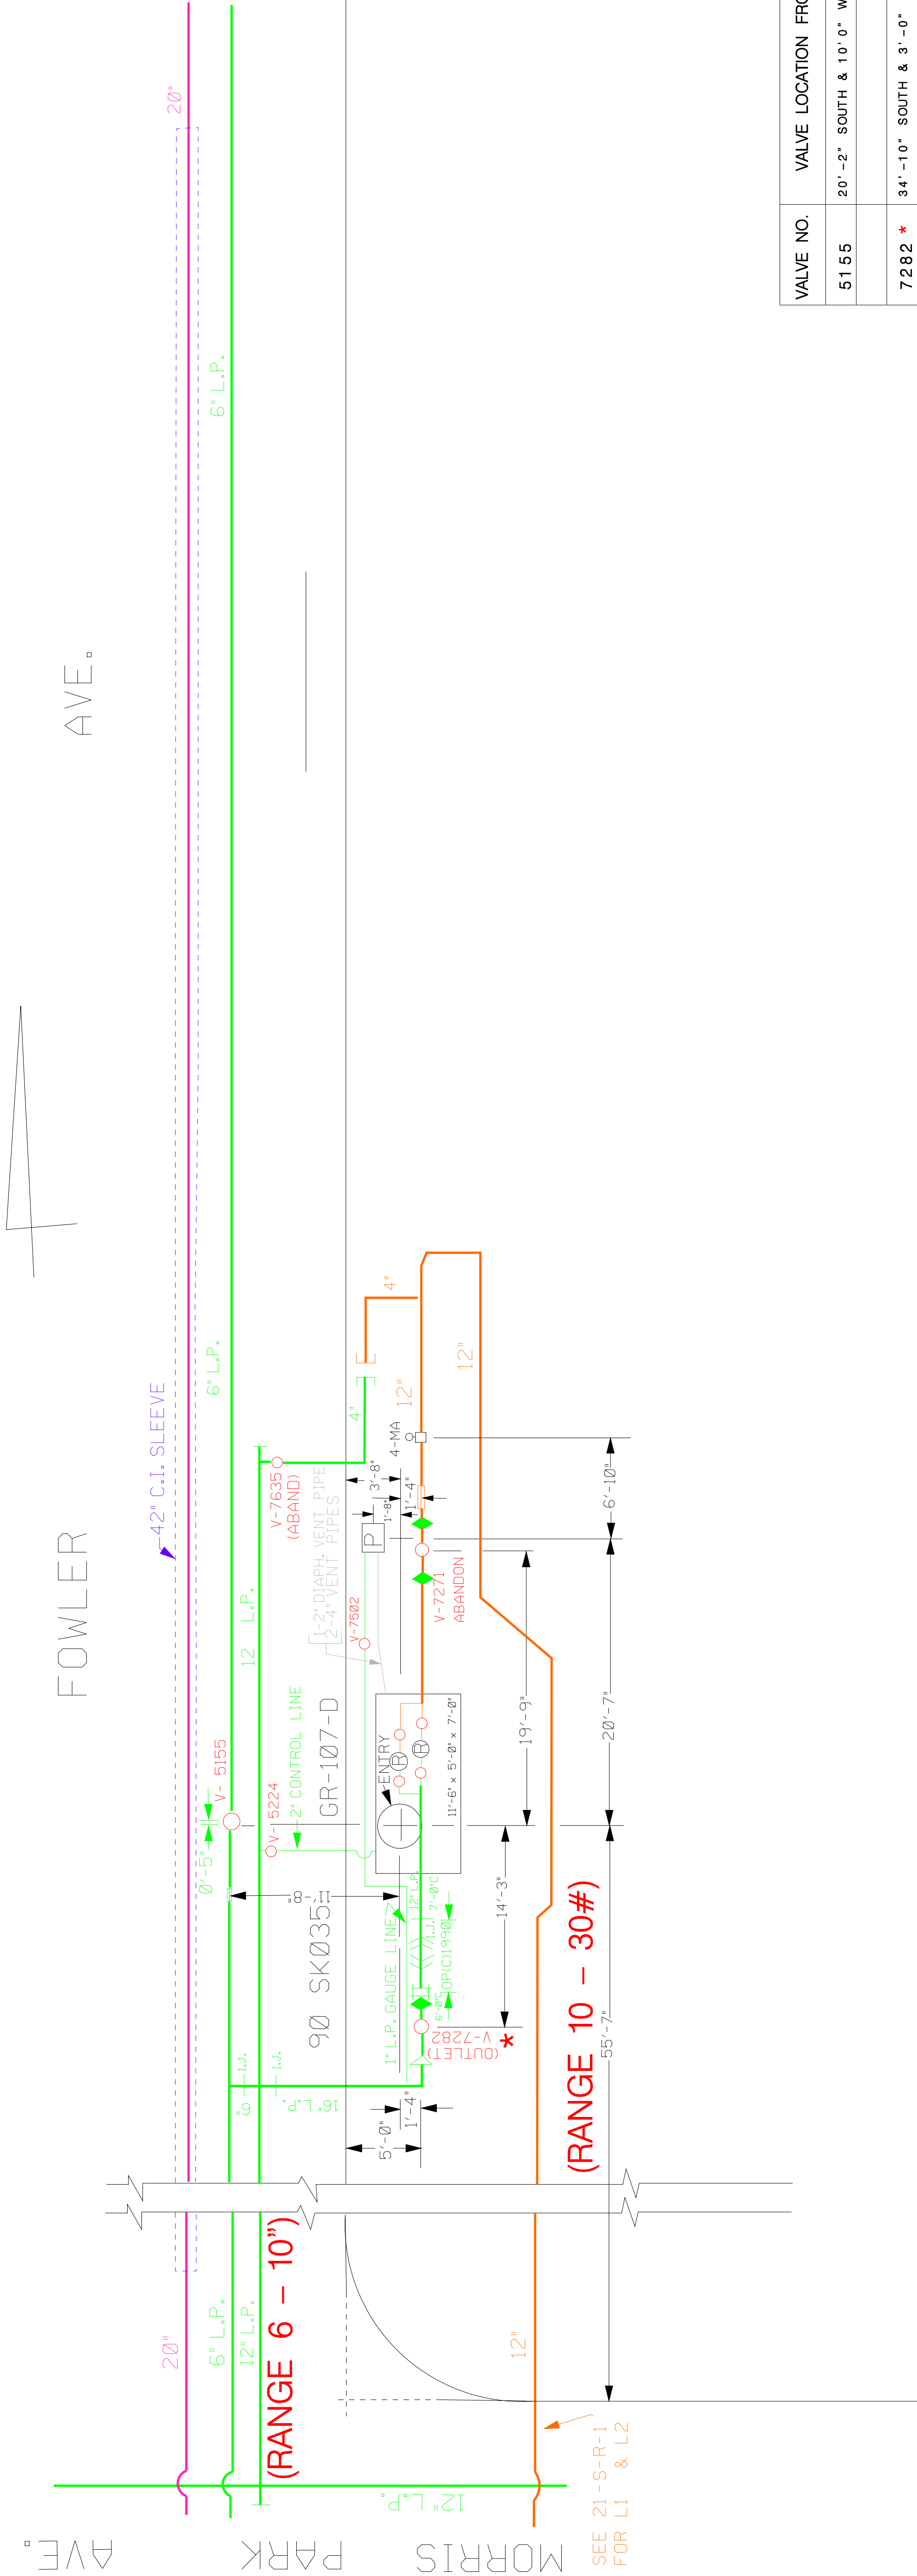


GAS REGULATOR PLATE

PLATE NO. 21-S-R

[illegible][illegible]

- * = PRINCIPAL STATION VALVE INSPECTED AND PARTIALLY OPERATED ANNUALLY.
- + = TRANSMISSION VALVE (ANY VALVE THAT SEES PRESSURE ABOVE 125 PSIG) INSPECTED AND PARTIALLY OPERATED ANNUALLY.

ANY VALVE OPERATION OR MAINS CUT OUT IN THE AREA SHOWN ABOVE MAY AFFECT OPERATION OF THIS DISTRICT REGULATOR. THE CENTRAL GAS CONTROLLER AND THE MANAGER OF PRESSURE CONTROL MUST BE NOTIFIED IN ADVANCE OF THIS WORK.

[illegible]