
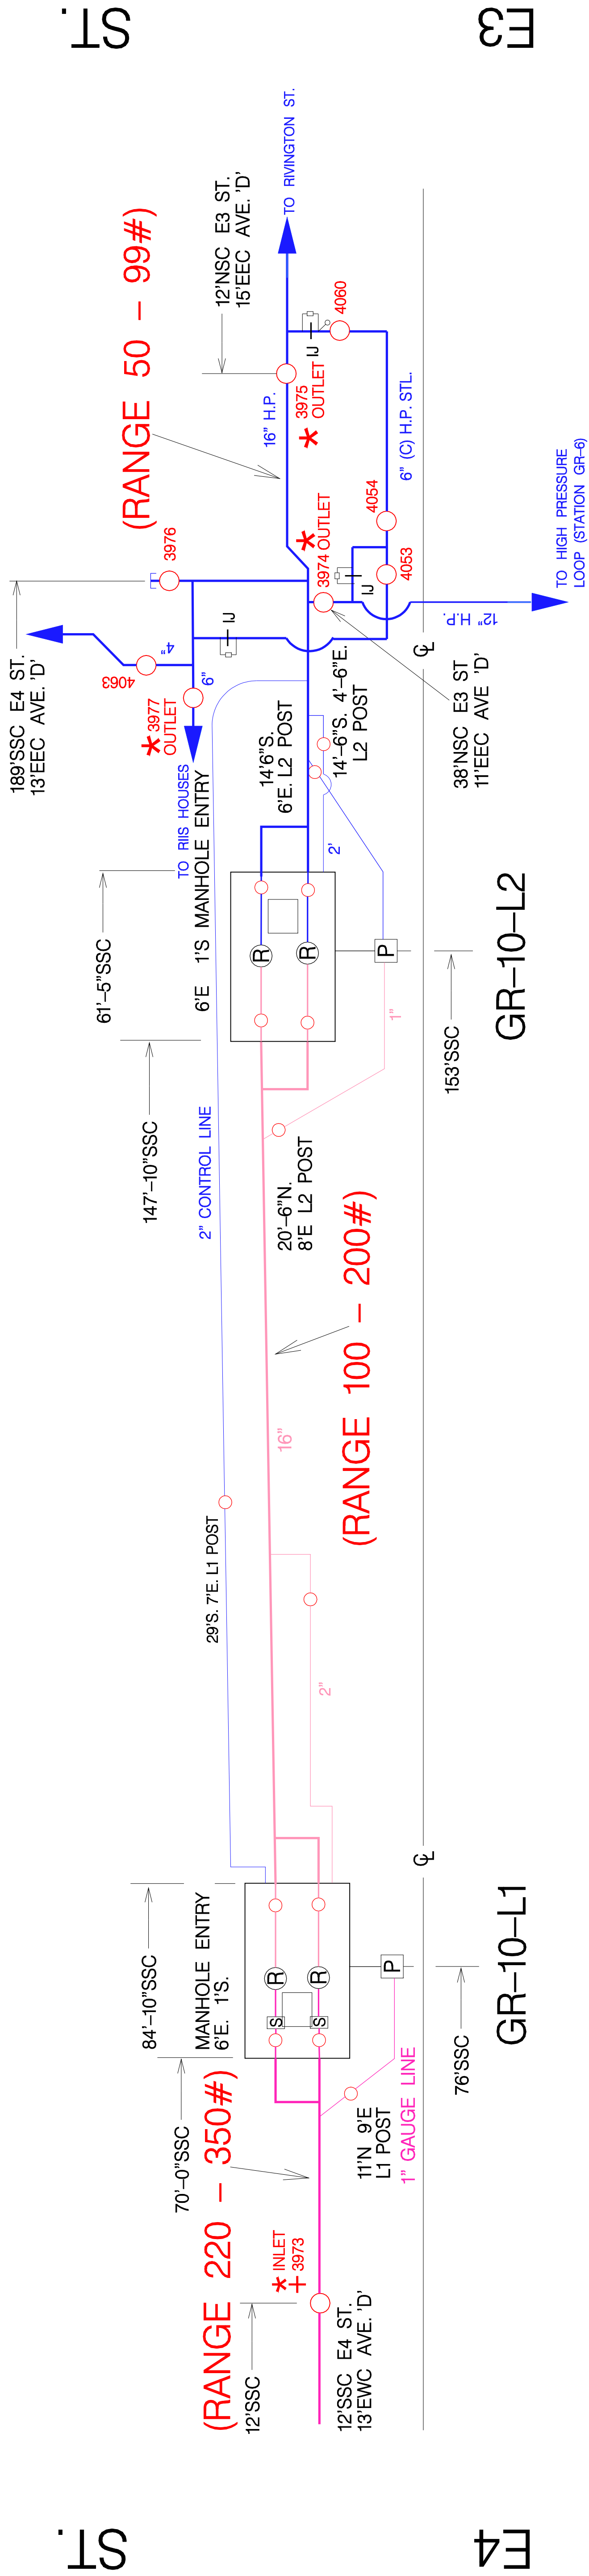


GAS REGULATOR PLATE - GR10

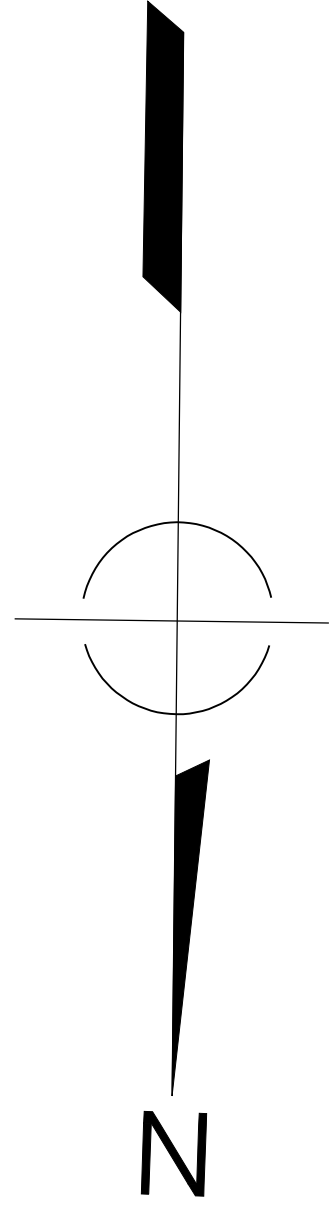

AVE.

ס'

VALVE NO.	VALVE LOCATION	FROM	GAUGE POST
3973	★ +	63' N. L1 – 10'–6" E.	L1 POST
3974	★	63'–8"S. L2 – 8'–0"E.	L2 POST
3975	★	86'–8"S. L2 – 14'–0"E.	L2 POST
3976		68'–0"S. L2 – 15'–0"E.	L2 POST
3977	★	30'S L2 – 12'E	L2 POST
4063		6' NNC of E. 3 ST. & 15' EEC	of AV. D

GAS REGULATOR STATION													
DATA ON VALVES WITHIN THE MANHOLES						DATA ON VALVES OUTSIDE THE MANHOLES							
VALVE NO.	SIZE	VALVE MANUF.	VALVE TYPE	FIG. OR MODEL NO.	TURNS TO OPEN	NORMAL POSITION	VALVE NO.	SIZE	VALVE MANUF.	VALVE TYPE	FIG. OR MODEL NO.	TURNS TO OPEN	NORMAL POSITION
L1-1	8"	GROVE	BALL			OPEN	3971	16"		BALL		64.5-L	OPEN
L1-2	8"	GROVE	BALL			OPEN	3972	16"		BALL		64.5-L	OPEN
L1-3	8"	GROVE	BALL			OPEN	3973 ✖ +	16"		BALL	INLET	64.5-L	OPEN
L1-4	8"	GROVE	BALL			OPEN	3974 ✖	12"		BALL	OUTLET	16.5-L	OPEN
L2-1	8"	GROVE	BALL			OPEN	3975 ✖	16"		BALL	OUTLET	64.5-L	OPEN
L2-2	8"	GROVE	BALL			OPEN	3976	12"		BALL		16.5-L	CLOSED
L2-3	8"	ORBIT	BALL			OPEN	3977 ✖	6"		BALL	OUTLET	0.25-L	OPEN
L2-4	8"	ORBIT	BALL			OPEN	4063	4"		PLUG		0.25-L	OPEN
LOCATION: AVE. 'D' bet. E3 ST. & E4 ST.												GR-10	
OPERATING MAP: 14-N							GENERAL MAINS MAP:						

STRAINER INFORMATION				
	SIZE	BODY RATING	MANUFACTOR	MODEL
S-1	8"	300	APOLLO	BASKET
S-2	8"	300	APOLLO	BASKET

ANY VALVE OPERATION OR MAINS CUT OUT IN THE AREA SHOWN ABOVE MAY AFFECT OPERATION OF THIS DISTRICT REGULATOR. THE CENTRAL GAS CONTROLLER AND THE MANAGER OF PRESSURE CONTROL MUST BE NOTIFIED IN ADVANCE OF THIS WORK.

- * = PRINCIPAL STATION VALVE
INSPECTED AND PARTIALLY
OPERATED ANNUALLY.
- + = TRANSMISSION VALVE
(ANY VALVE THAT SEES
PRESSURE ABOVE 125 PSIG)
INSPECTED AND PARTIALLY
OPERATED ANNUALLY.

[illegible]