


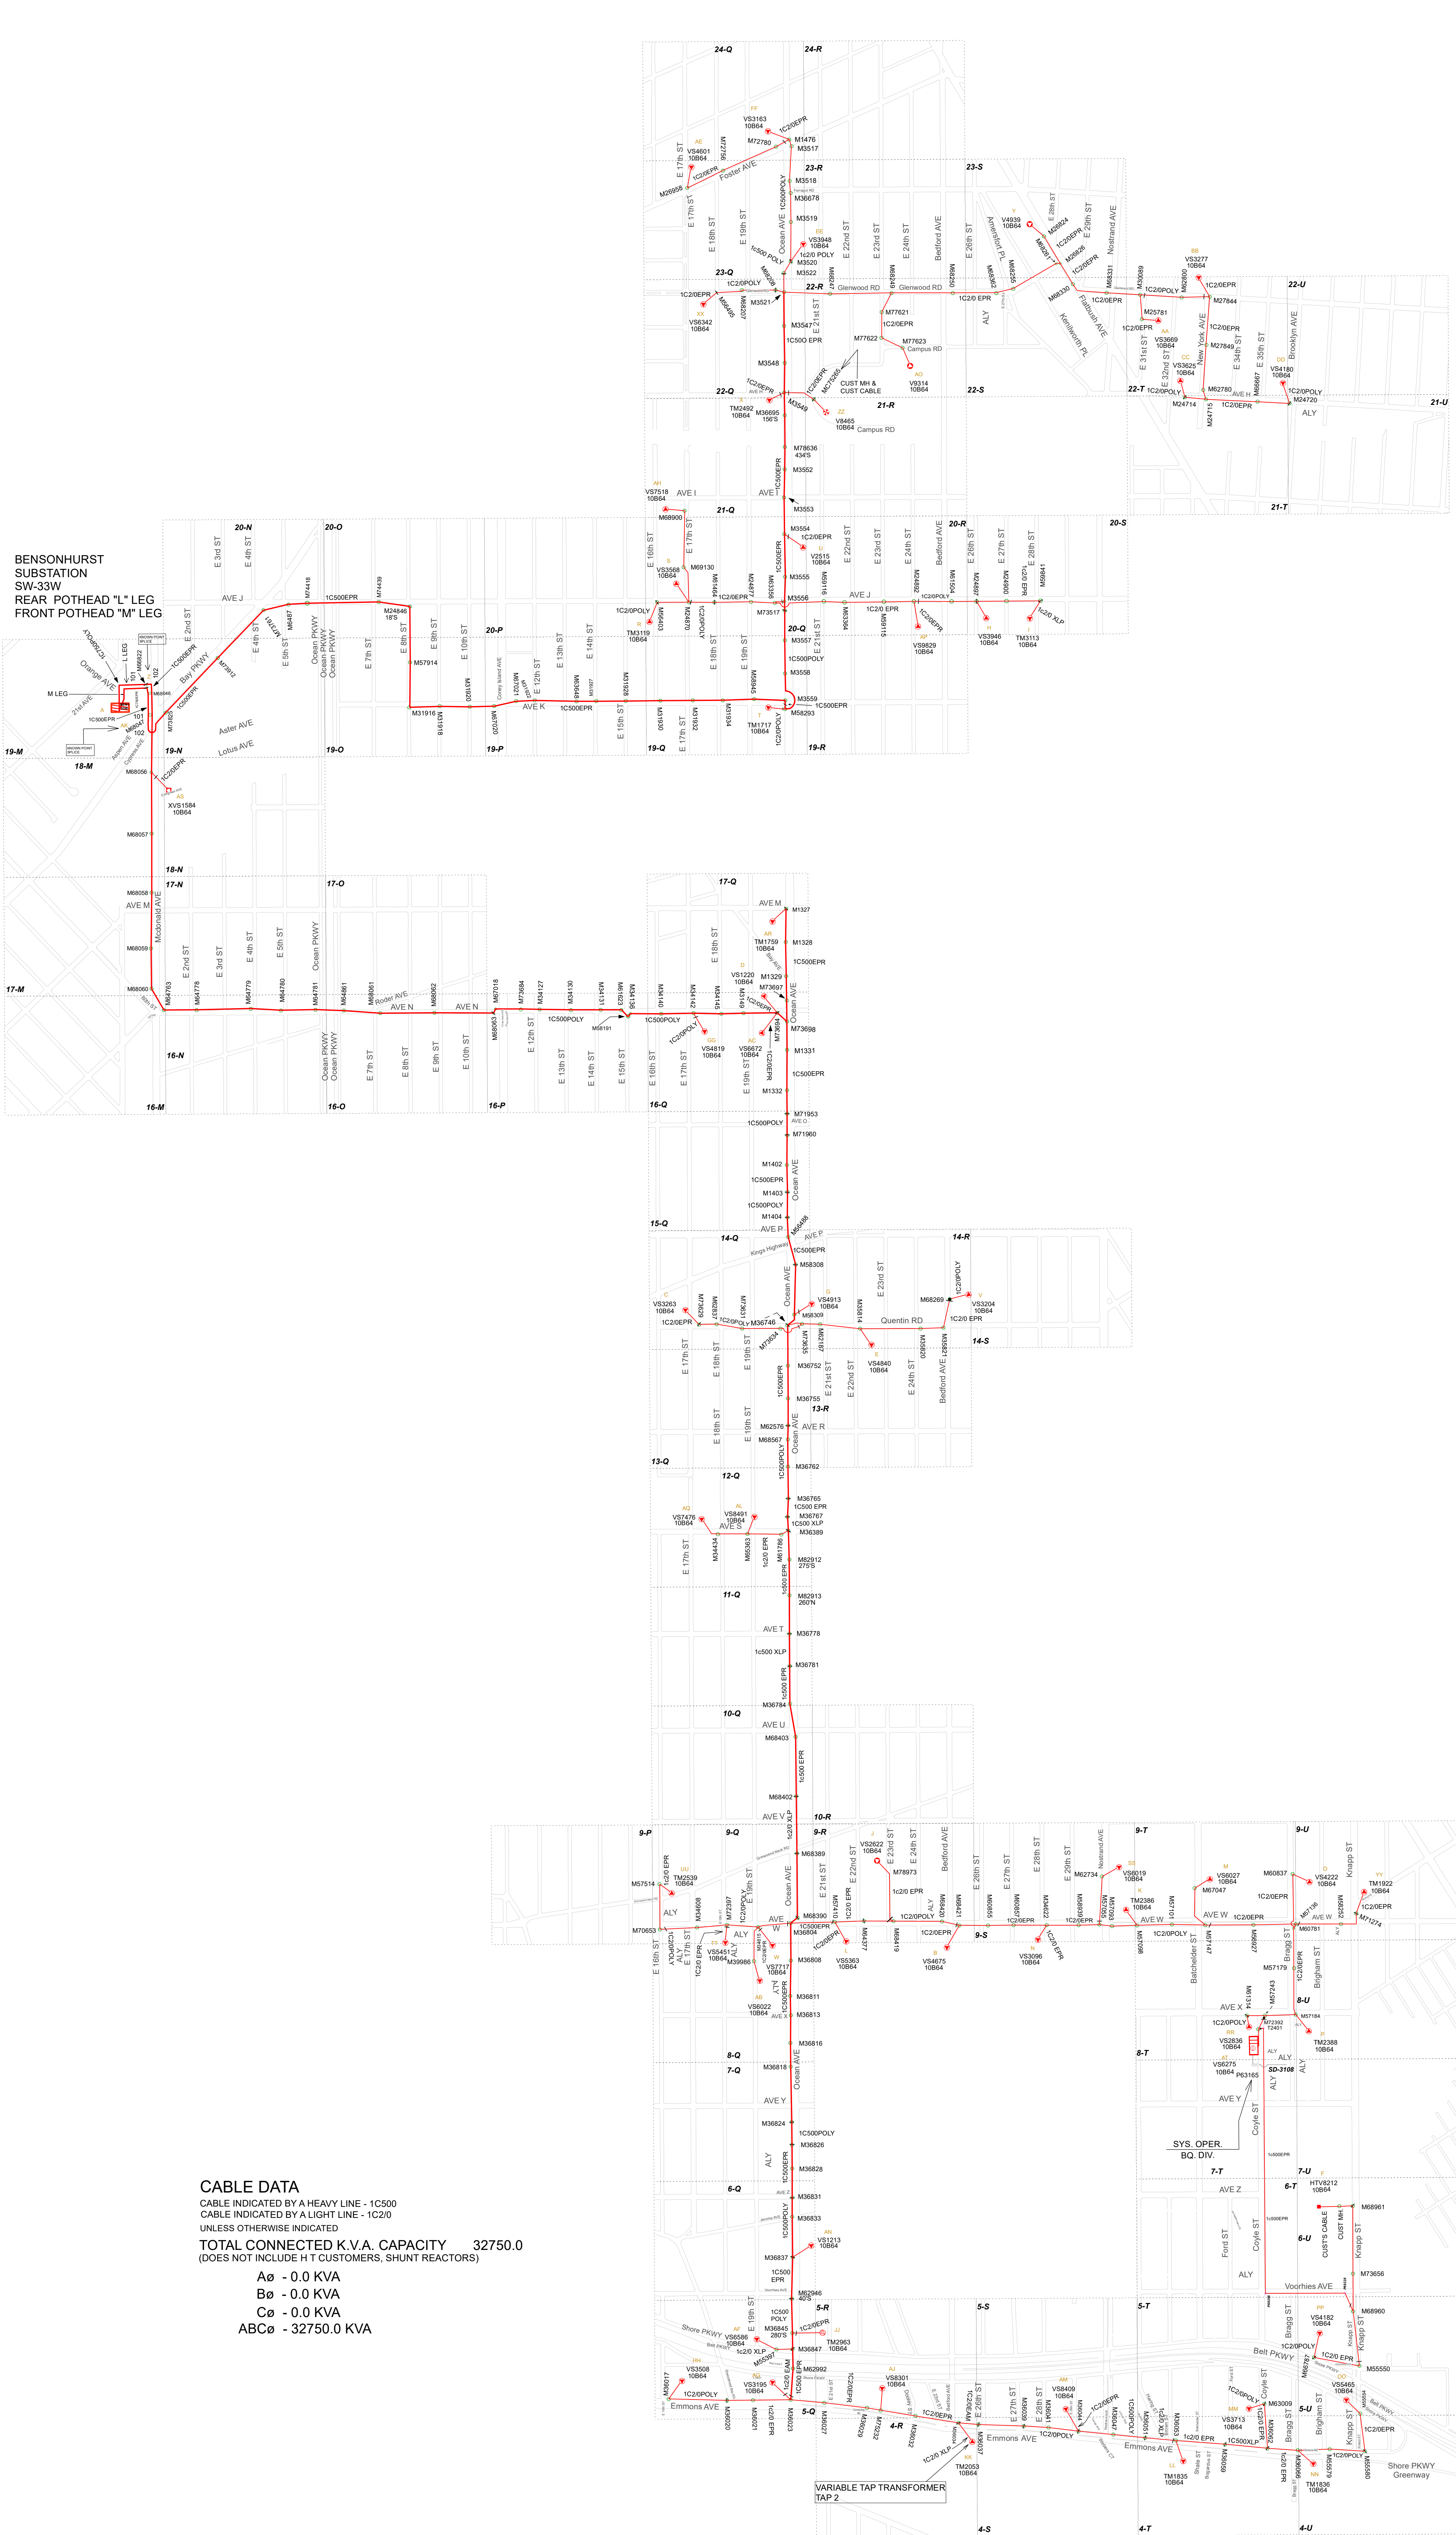

V OR TM NO	LOCATION	N O T E	AREA	EQUIP	V OR TM NO	LOCATION	N O T E	AREA	EQUIP
AL	VS B E 19TH ST E.S. 31' NO AVE S SDWK. GRTG.	E	12-Q	500 F S Y	A	VS B 33W BENI SUBSTATION	E	19-M	
AM	VS B EMMONS AVE N.S. 22' W/O E 20TH ST SDWK. GRTG.	E	5-S	500 F S Y	B	VS B 4675 B AVE W E S 37' W/O BEDFORD AVE SDWK. GRTG.	E	8-R	500 F S Y
AN	VS B OCEAN AVE E.S. 283' NO VOORNIES AVE SDWK. GRTG.	E	6-Q	500 F S Y	C	VS B E 17TH ST E.S. 38' NO QUENTIN RD SDWK. GRTG.	E	14-Q	500 F S Y
AO	V B BROOKLYN COLLEGE CAMPUS RD NO S.S. 261' W/O E 23RD ST SDWK. GRTG. 18665 <-----> 18668 V-5380 SPOT NM X V-5225 <-----> V-5151 18667 <-----> 18670 18664 <-----> 18670 SPOT NN 18664 <-----> 18664	E	1000 F S Y	22-R	D	VS B AVE N S.S. 100' W/O OCEAN AVE SDWK. GRTG.	E	16-Q	500 F S Y
AP	VS B AVE J S.S. 39' E/O E 24TH ST SDWK. GRTG.	E	20-R	500 F S Y	E	VS B QUENTIN RD S.S. 38' E/O E 22ND ST SDWK. GRTG.	E	14-R	500 F S Y
AQ	VS B AVE S N S 207' W/O E 18TH ST SDWK. GRTG.	E	12-Q	500 F S Y	F	HTV B 8212 CONEY ISLAND WATER POLLUTION CONTROL PLANT KNAPP ST & AVE Z PAD MOUNTED ON PRIV. PROP IN PLANT FOR ACCESS CALL 718-891-4000 18668 <-----> 18661 HTV-8212 <-----> HTV-8212 187 <-----> 183 18664 <-----> 18664 18662 <-----> 18665 HTV-8212 <-----> HTV-8212 182 <-----> 182	6-U	30	500 F S Y
AR	TM B AVE M CENTER 22' W/O OCEAN AVE SUBMERSIBLE UNIT	E	17-Q	500 F S Y	G	VS B OCEAN AVE E.S. 35' NO QUENTIN RD SDWK. GRTG.	E	14-R	500 F S Y
AS	XVS B MCDONALD AVE E.S. 574' S/O BAY PARKWAY SDWK. GRTG. SHUNT REACTOR	18-A	1000 F S Y	SHUNT REACTOR	H	VS B AVE J S.S. 22E E 20ND ST SDWK. GRTG.	E	20-S	500 F S Y
AT	VS B COYLE ST W.S. 327' S/O AVE X SDWK. GRTG.	250Y 27 KV/4 KV F S Y	8-T		I	TM B E 28TH ST E.S. 29' S/O AVE J	E	20-S	500 F S Y
BB	VS B NEW YORK AVE W.S. 35' NO GLENWOOD RD SDWK. GRTG.	E	22-T	500 F S Y	J	VS B 2200 GRAVESEND NECK ROAD E 23RD ST W.S.	E	9-R	1000 F S Y
CC	VS B AVE H N.S. 42' W/O B'KLYN AVE SDWK. GRTG. 18664 <-----> 18669 SPOT NN 18664 <-----> 18669 VS-3417 VS-3508	E	22-T	500 F S Y	K	TM B AVE W S.S. 208' E/O NOSTRAND AVE	E	9-S	500 F S Y
DD	VS B AVE H N.S. 42' W/O B'KLYN AVE SDWK. GRTG.	E	22-T	500 F S Y	L	VS B AVE W S.S. 102' E/O E 21 ST SDWK. GRTG.	E	9-R	500 F S Y
EE	VS B OCEAN AVE E.S. 267' NO GLENWOOD RD SDWK. GRTG.	E	23-Q	500 F S Y	M	VS B BATCHELDER ST E.S. E 23RD ST W.S.	E	9-T	500 F S Y
FF	VS B FOSTER AVE N.S. 34' W/O OCEAN AVE SDWK. GRTG.	E	24-Q	500 F S Y	N	VS B E 28TH ST E.S. 38' S/O AVE W SDWK. GRTG.	E	9-S	500 F S Y
GG	VS B AVE N S.S. 44' E/O E 17TH ST SDWK. GRTG.	E	16-Q	500 F S Y	O	VS B BRAGG ST E.S. 362' NO AVE W SDWK. GRTG.	E	9-U	500 F S Y
HH	VS B EMMONS AVE N.S. 42' E/O E 16TH ST SDWK. GRTG.	E	5-Q	500 F S Y	P	TM B AVE X S.S. 40' E/O BRAGG ST	E	8-U	500 F S Y
JJ	TM B OCEAN AVE E.S. 39' NO SHORE PKWY NO SERVICES RD SUBMERSIBLE	E	5-R	750 F S Y	R	VS B E 16TH ST E.S. 29' S/O AVE J	E	20-Q	500 F S Y
KK	TM B EMMONS AVE NORTH ROADWAY C78E BEDFORD AVE SUBMERSIBLE UNIT VARIABLE TAP TRANSFORMER	E	4-R	500 F S Y	S	VS B E 17TH ST W.S. 65' NO AVE J SDWK. GRTG. 18664 <-----> 18661 SPOT NM 18664 <-----> 18662 VS-3716 VS-3655	20-Q		500 F S Y
LL	TM B EMMONS AVE CENTER 44' E/O BROWN ST	E	4-T	500 F S Y	T	TM B AVE K N.S. 26' W/O OCEAN AVE SUBMERSIBLE UNIT VARIABLE TAP TRANSF TAP 2 - NEUTRAL	E	19-Q	500 F S Y
MM	VS B COYLE ST W.S. FO 2800 COYLE ST NO EMMONS AVE SLY SDWK. GRTG. 18664 <-----> 18667 VS-3681 VS-3681	E	5-T	500 F S Y	U	V B NEW YORK TELEPHONE CO 1421 OCEAN AVE SLY SDWK. GRTG. 18664 <-----> 18665 V-2686	20-Q		500 F S Y
NN	TM B EMMONS AVE NORTH ROADWAY CENTER 52' E/O BRAGG ST	E	4-U	500 F S Y	V	VS B JAMES MADISON HS BEDFORD AVE E.S. 235' NO QUENTIN RD SLY SDWK. GRTG. 18664 <-----> 18667 VS-3301	14-R		500 F S Y
OO	VS B SHORE PKWY SOUTH SERVICE RD S20V KNAPP ST ELY SDWK. GRTG. 18664 <-----> 18667 SPOT NM 18664 <-----> 18668 VS-5318 VS-5165	E	5-U	500 F S Y	W	VS B AVE W S.S. 59' E/O E 19TH ST SDWK. GRTG.	E	8-Q	500 F S Y
PP	VS B SHORE PKWY NORTH SERVICE RD N 137' E/O BRAGG ST SDWK. GRTG.	E	5-U	500 F AT Y	X	TM B AVE H S.S. 25' W/O OCEAN AVE SDWK. GRTG. SUBMERSIBLE	E	21-Q	500 F S Y
RR	VS B SHEEPSHEAD BAY HS 2908-3000 AVE X CENTER SDWK. GRTG. E 18664 <-----> 18661 SPOT NM 18664 <-----> 18662 VS-3914 VS-1693	E	6-T	500 F I Y	Y	V B MCDONALD AVE W.S. 230' NO BAY PKWAY. ON WALK 18664 <-----> 18661 VS-3825 VS-3825	23-S		1000 F S Y
SS	VS B NOSTRAND AVE E.S. 380' NO AVE W SDWK. GRTG.	E	9-S	500 F S Y	Z	VS B E 31 ST W.S. 208' S/O GLENWOOD RD SDWK. GRTG.	E	22-T	500 F S Y
TT	VS B E 16TH ST E438 AVE W SDWK. GRTG.	E	9-Q	500 F S Y	AA	VS B AVE N S.S. 43' W/O OCEAN AVE SDWK. GRTG.	E	8-Q	500 F S Y
UU	TM B E 16TH ST W.S. 67' NO GRAVESEND NECK RD	E	9-Q	500 F S Y	AC	VS B AVE N S.S. 43' W/O OCEAN AVE SDWK. GRTG.	E	16-Q	500 F S Y
XX	VS B GLENWOOD RD S31W E 18TH ST SDWK. GRTG.	E	22-Q	500 F S Y	AE	VS B E 17TH ST E.S. 41' NO FOSTER AVE SDWK. GRTG.	E	23-Q	500 F S Y
YY	TM B WHITNEY AVE S.S. 39' E/O KNAPP ST	E	9-U	500 F AT Y	AF	VS B E 19TH ST E.S. 22' NO SHORE PKWY SDWK. GRTG.	E	5-Q	500 F S Y
ZZ	V B CHILLER PLANT 1301 OCEAN AVE CAMPUS RD W.S. 250' S/O AVE H 18664 <-----> 18663 SPOT NM 18664 <-----> 18665 VS-7493 VS-7995 18666	E	21-R	2500 F S Y	AG	VS B OCEAN AVE W.S. 44' NO EMMONS AVE SDWK. GRTG.	E	5-Q	500 F S Y
					AH	VS B AVE I S.S. 74' W/O E 17TH ST SDWK. GRTG.	E	21-Q	500 F S Y
					AJ	VS B CAMBRIDGE HOUSE EMMONS AVE N.S. 404' E/O E 21 ST 2ND WLY SDWK. GRTG. 150 NM 18664 <-----> 18663 VS-7459 VS-7459 18663	5-R	25	500 F S Y
					AK	M B MCDONALD AVE W.S. 23' W/O BAY PKWAY. ON WALK 18664 <-----> 18661 VS-3806 VS-3825	19-M		KNOWN POINT SPLICE

