


WHITE PLAINS NETWORK AREA MAP

(PART 1 OF 2)

	8W62		8W94
	8W63		8W95
	8W64		8W97
	8W65		
	8W66		
	8W67		
	8W68		
	8W69		
	8W70		
	8W71		
	8W72		
	8W73		
	8W74		
	8W75		
	8W76		
	8W77		
	8W79		
	8W80		
	8W81		
	8W82		
	8W84		
	8W85		
	8W88		
	8W90		
	8W91		
	8W92		
	8W93		

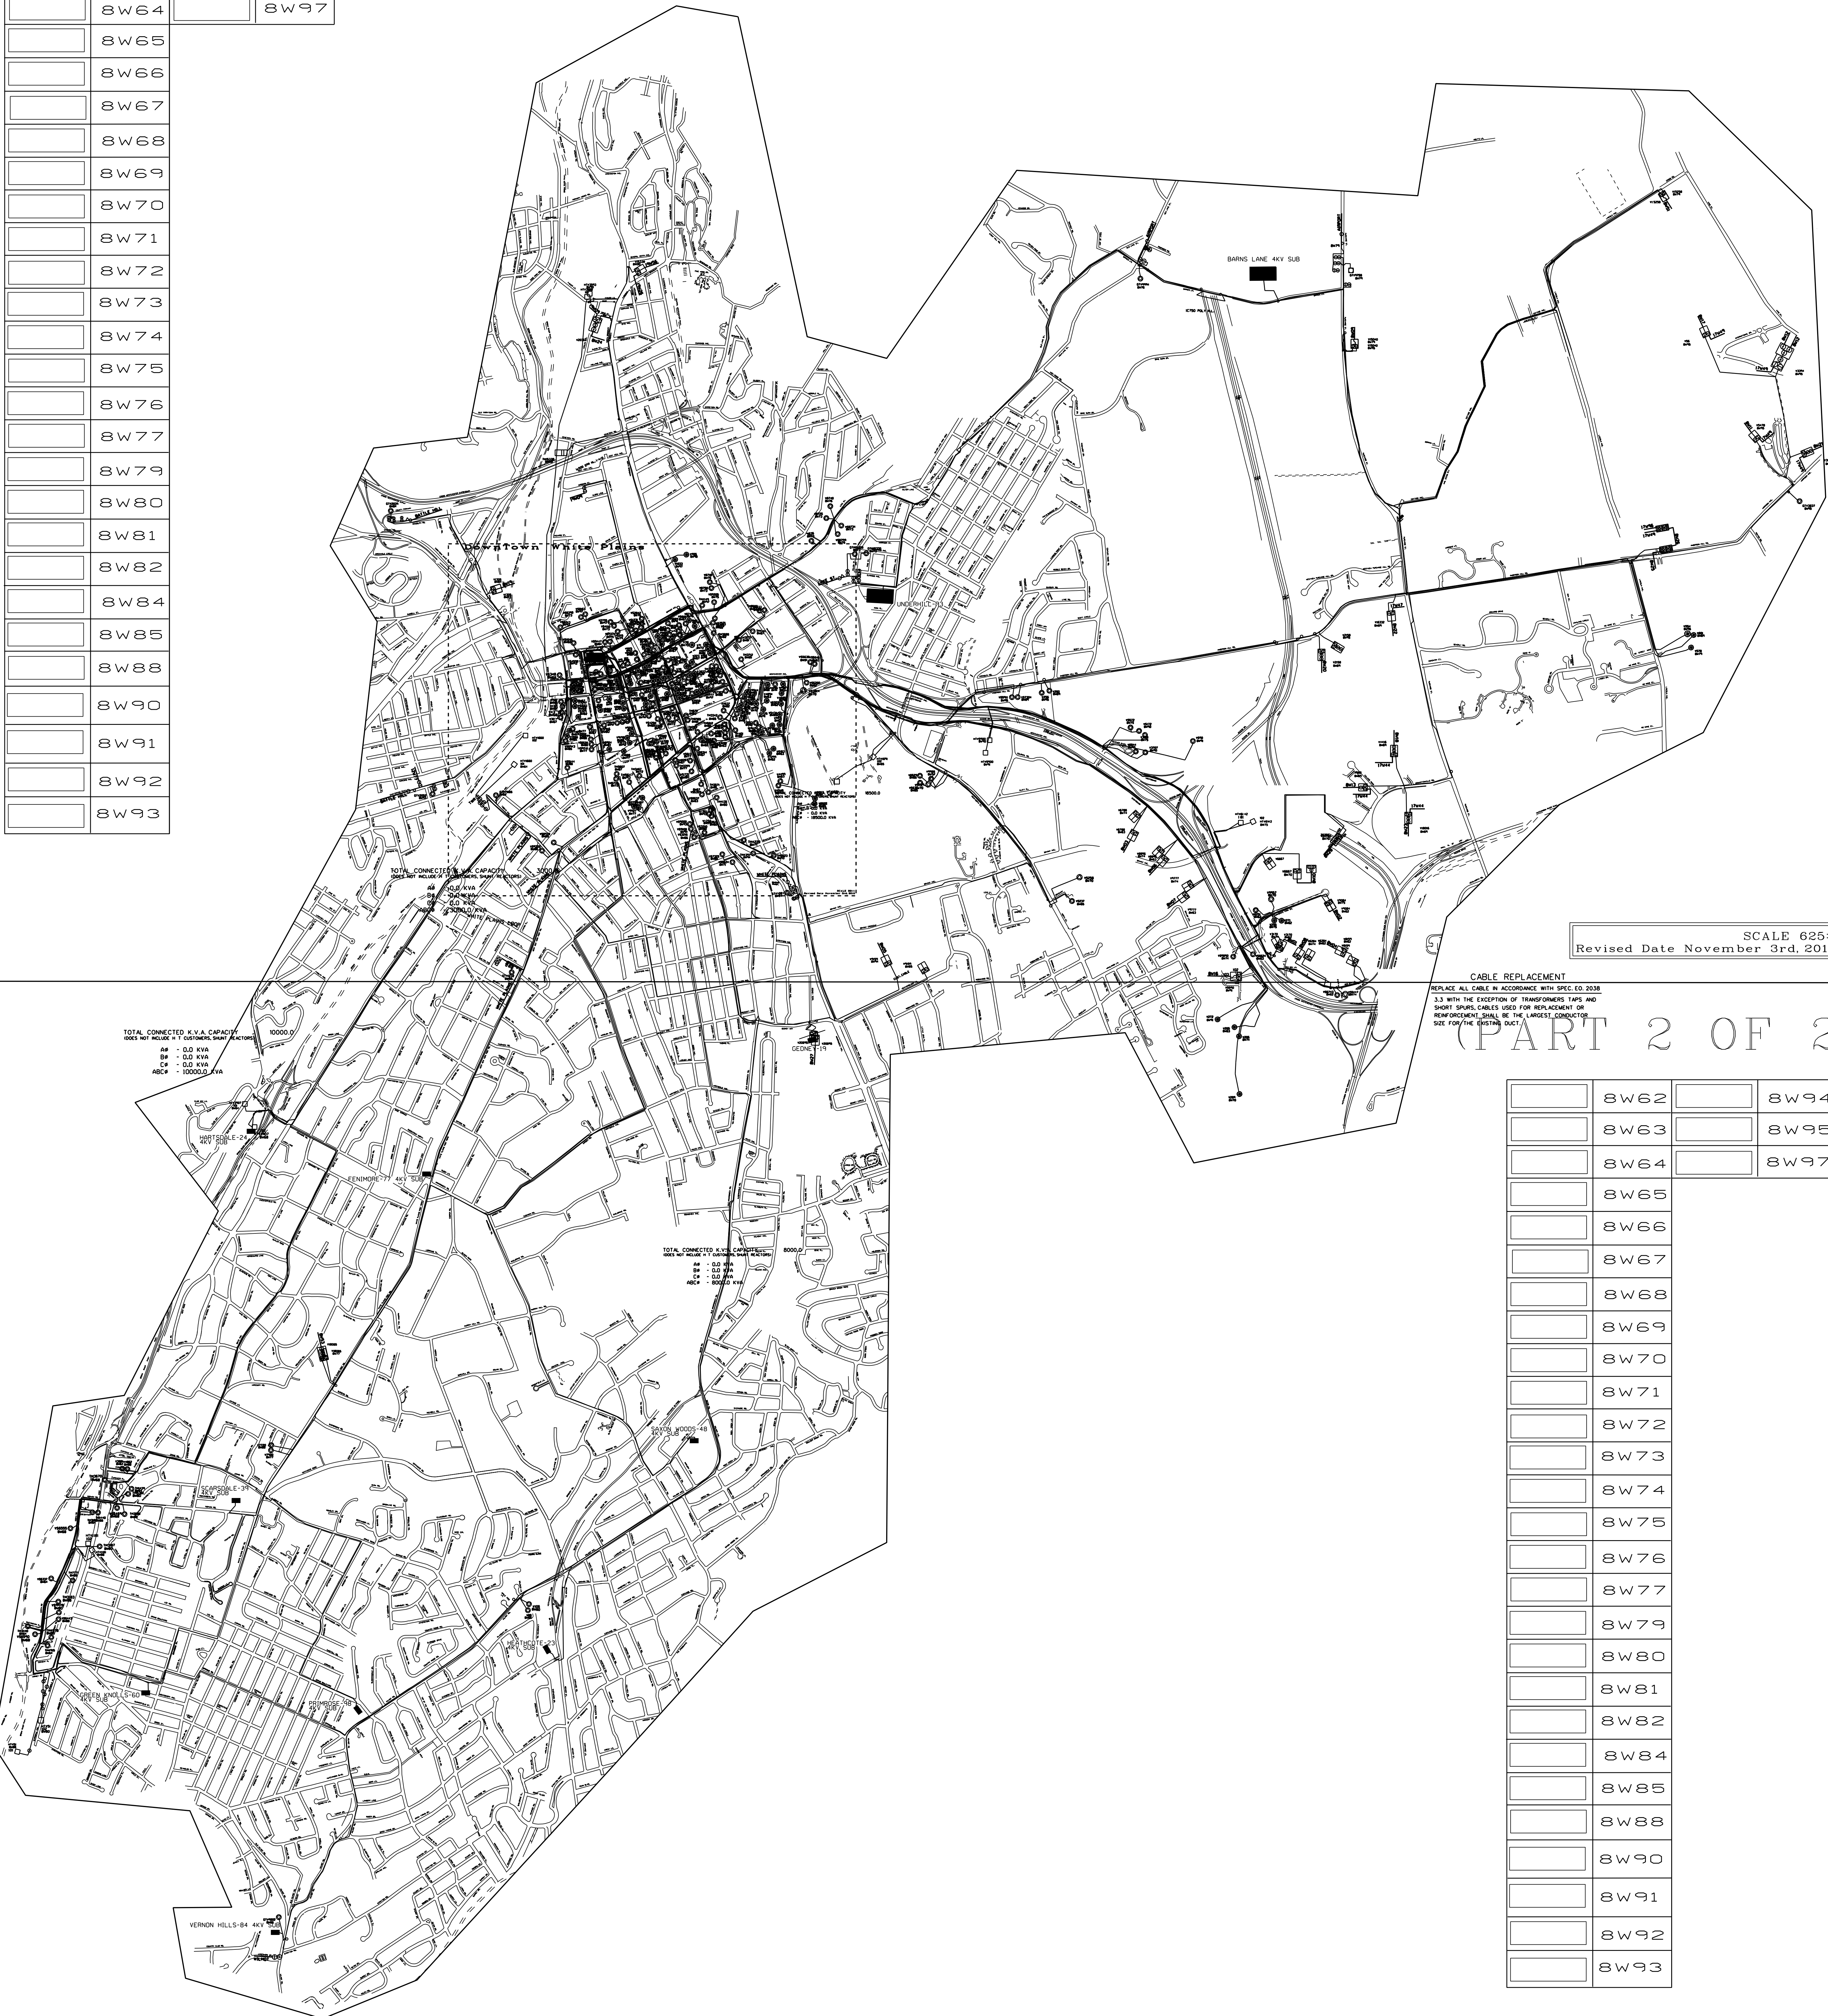

SCALE 625:1
Revised Date November 3rd, 2015

CABLE REPLACEMENT
REPLACE ALL CABLE IN ACCORDANCE WITH SPEC. EQ. 2038
3.3 WITH THE EXCEPTION OF TRANSFORMER TAPS AND
SHORT SPURS. CABLES USED FOR REPLACEMENT OR
REINFORCEMENT SHALL BE THE LARGEST CONDUCTOR
SIZE FOR THE EXISTING DUCT.

(PART 2 OF 2)

	8W62		8W94
	8W63		8W95
	8W64		8W97
	8W65		
	8W66		
	8W67		
	8W68		
	8W69		
	8W70		
	8W71		
	8W72		
	8W73		
	8W74		
	8W75		
	8W76		
	8W77		
	8W79		
	8W80		
	8W81		
	8W82		
	8W84		
	8W85		
	8W88		
	8W90		
	8W91		
	8W92		
	8W93		

WHITE PLAINS NETWORK AREA MAP

SCALE 625:1
Revised Date November 3rd, 2015